


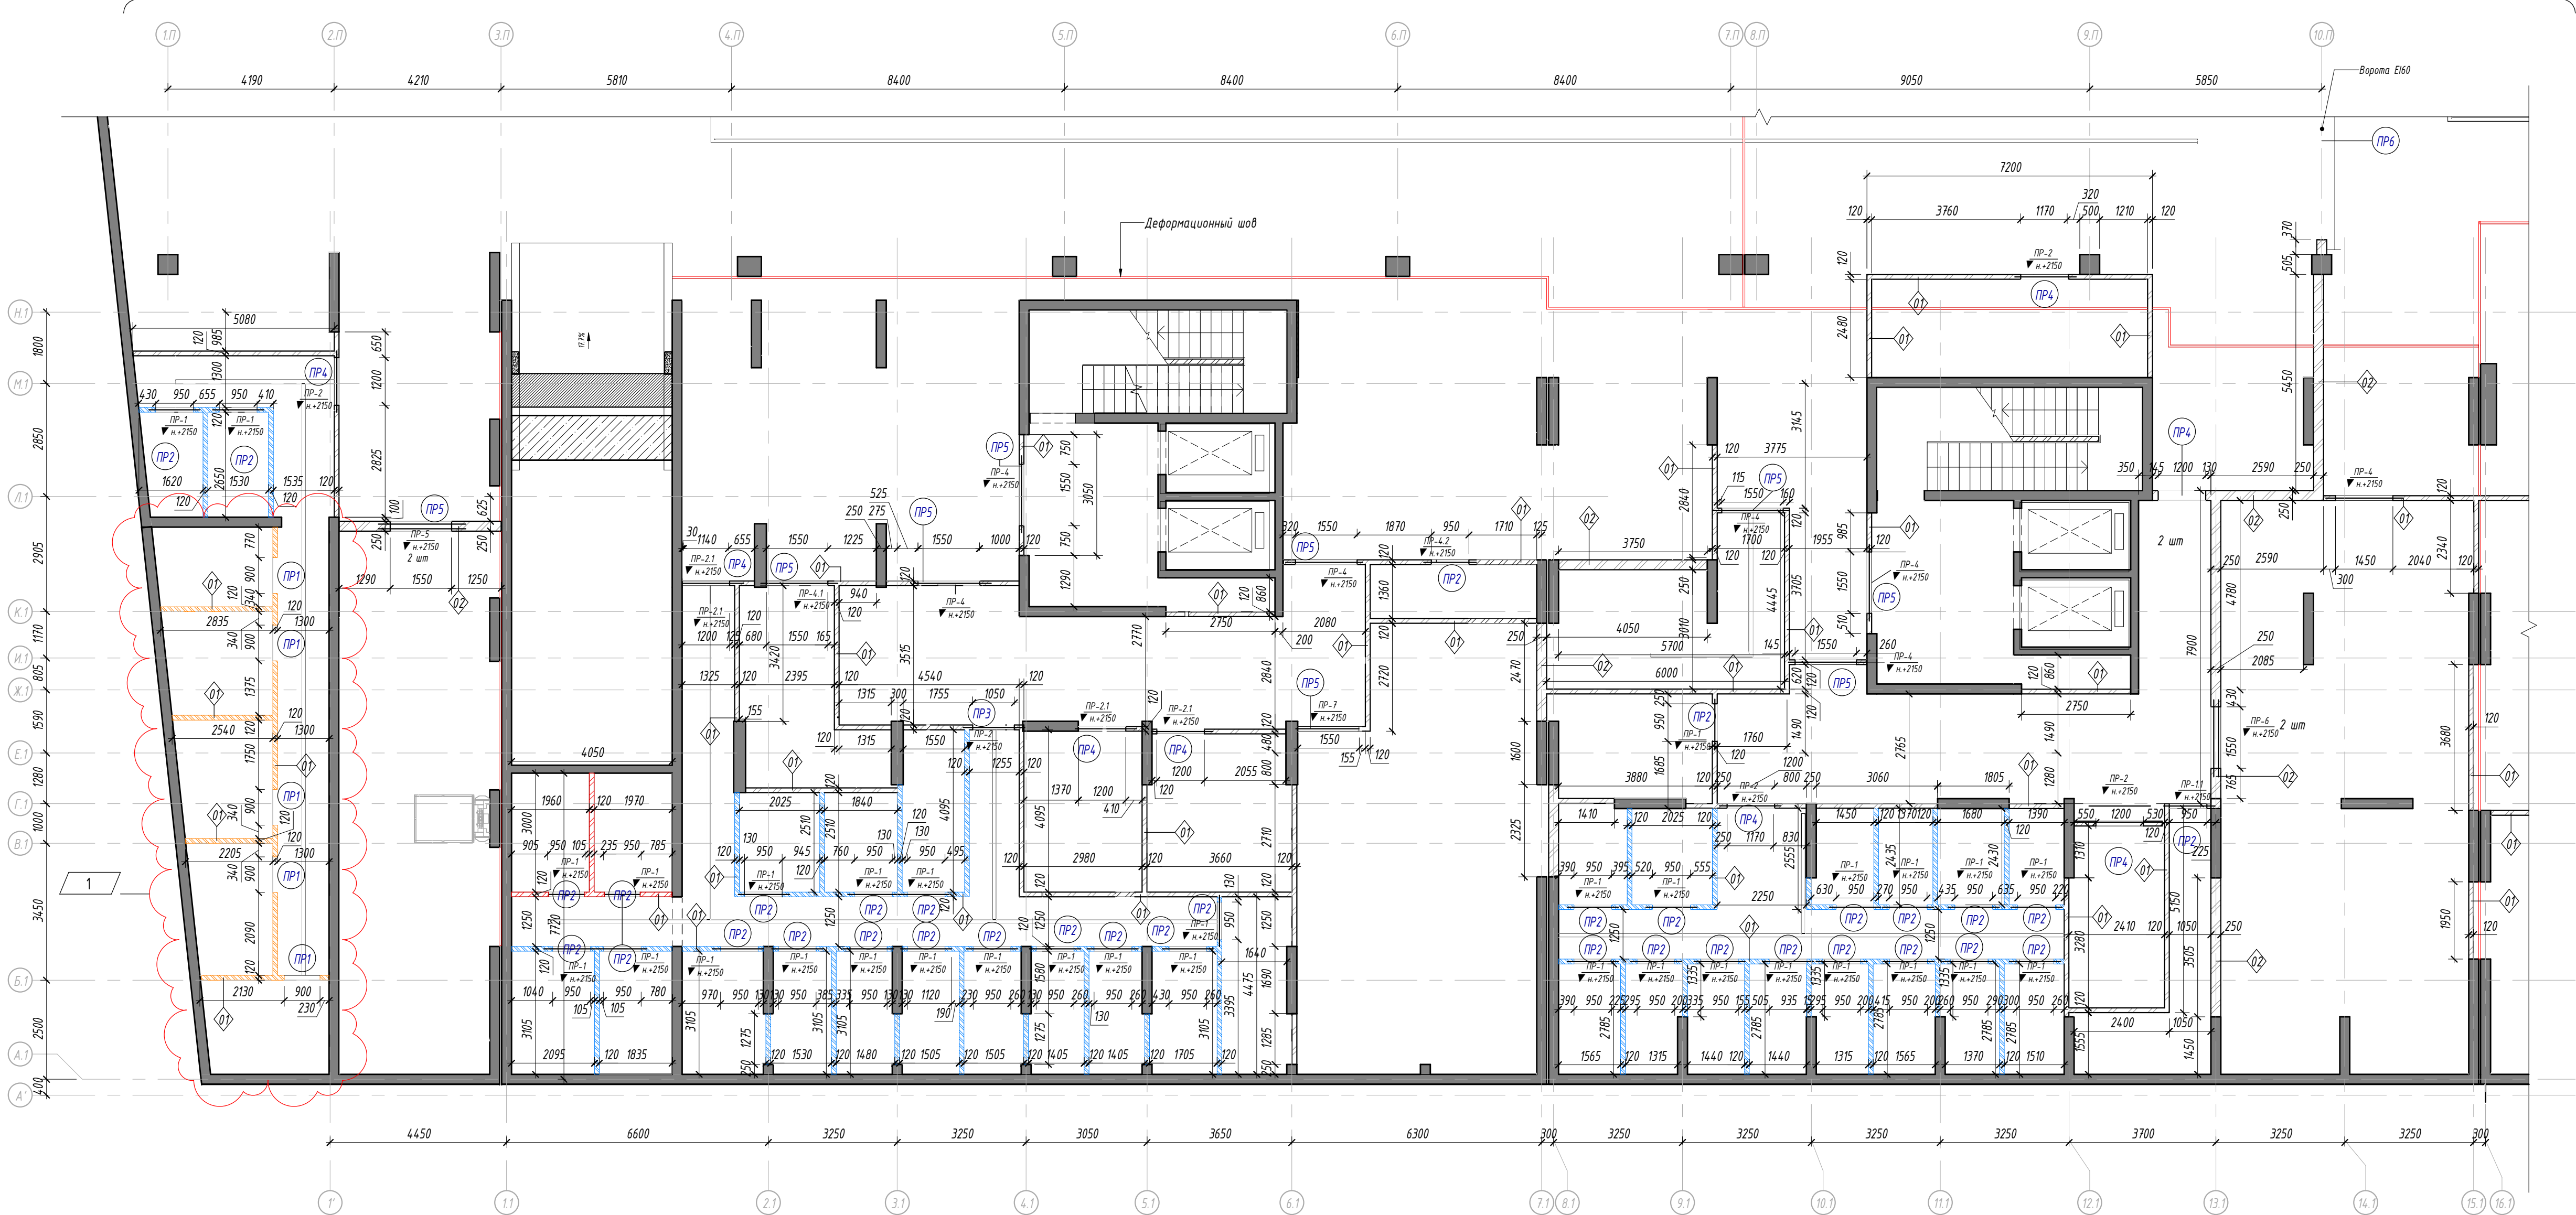

Фрагмент 3 лист 5


УСЛОВНЫЕ ОБОЗНАЧЕНИЯ

- Наружные и внутренние стены (пилоны, колонны): монолитный железобетон (см. Раздел КР);
- Перегородка из КР-р-по 250х120х65 1НФ/100/2,0/50/ГОСТ 530-2012 Кирпич полнотелый М100 на цем. песч. растворе М100 армированный стальной кладочной сеткой 50х50 через каждые 4 ряда кладки по ГОСТ 530-2012 толщиной 120 мм
- Стена из КР-р-по 250х120х65 1НФ/100/2,0/50/ГОСТ 530-2012 Кирпич полнотелый М100 на цем. песч. растворе М100 армированный стальной кладочной сеткой 50х50 через каждые 4 ряда кладки по ГОСТ 530-2012 толщиной 250 мм
- Утеплитель: экструзионный пенополистирол ТЕХНОНИКОЛЬ CARBON PROF или аналог - 50 мм
- Перегородка из КР-р-по 250х120х65 1НФ/100/2,0/50/ГОСТ 530-2012 Кирпич полнотелый М100 на цем. песч. растворе М100 армированный стальной кладочной сеткой 50х50 через каждые 4 ряда кладки по ГОСТ 530-2012 (h=2,50м. от чистого пола)
- Перегородка из КР-р-по 250х120х65 1НФ/100/2,0/50/ГОСТ 530-2012 Кирпич полнотелый М100 на цем. песч. растворе М100 армированный стальной кладочной сеткой 50х50 через каждые 4 ряда кладки по ГОСТ 530-2012 (h=2,37м. от чистого пола)
- Перегородка из КР-р-по 250х120х65 1НФ/100/2,0/50/ГОСТ 530-2012 Кирпич полнотелый М100 на цем. песч. растворе М100 армированный стальной кладочной сеткой 50х50 через каждые 4 ряда кладки по ГОСТ 530-2012 (h=2,05м. от чистого пола)
- Отметка чистого пола
- Обозначения сечений и разрезов
- Отверстия для прохождения инженерных коммуникаций в стенах или перегородках
- Маркировка перемычек
- отм. низа перемычки (дана от уровня ч.п. этажа)
- Маркировка проемов. Ведомость проемов см. на листе 20.
- Маркировка отверстий. Ведомость отверстий см. на листе 37.
- Деформационный шов
- Маркировка материалов перегородок. Ведомость см. на листе 10.

ПРИМЕЧАНИЕ

- Общие указания см. УМО-РД-АСО лист 01 Общие данные;
- Схему деления паркинга на фрагменты см. УМО-РД-АСО л. 02;
- Лист см. совместно с маркировочными планами УМО-РД-АР0 л. 4-7;
- Разрезы см. УМО-РД-АР0 л. 11;
- Ведомость отверстий, проемов, перемычек см. УМО-РД-АСО л. 08-09;
- Узлы примыкания кирпичных перегородок см. УМО-РД-АСО л. 015;
- Высотная отметка перемычек указана от уровня чистого пола этажа до низа перемычки (верха проема);
- Ведомость объемов кладки стен, ведомость элементов кладки стен см. УМО-РД-АСО л. 010;
- Узлы прохода коммуникаций см. УМО-РД-АР0 л. 24;
- См. совместно с альбомом КЖ-1, лист 11; КЖ-2, лист 13; КЖ-3, лист 13; КЖ-4, лист 1;
- Экспликация помещений см. на листах маркировочных планов альбом УМО-РД-АР0 л. 4-7;
- Размещение инженерных отверстий, маркировку, перемычки и привязки см. листы 011-013.

СХЕМА:

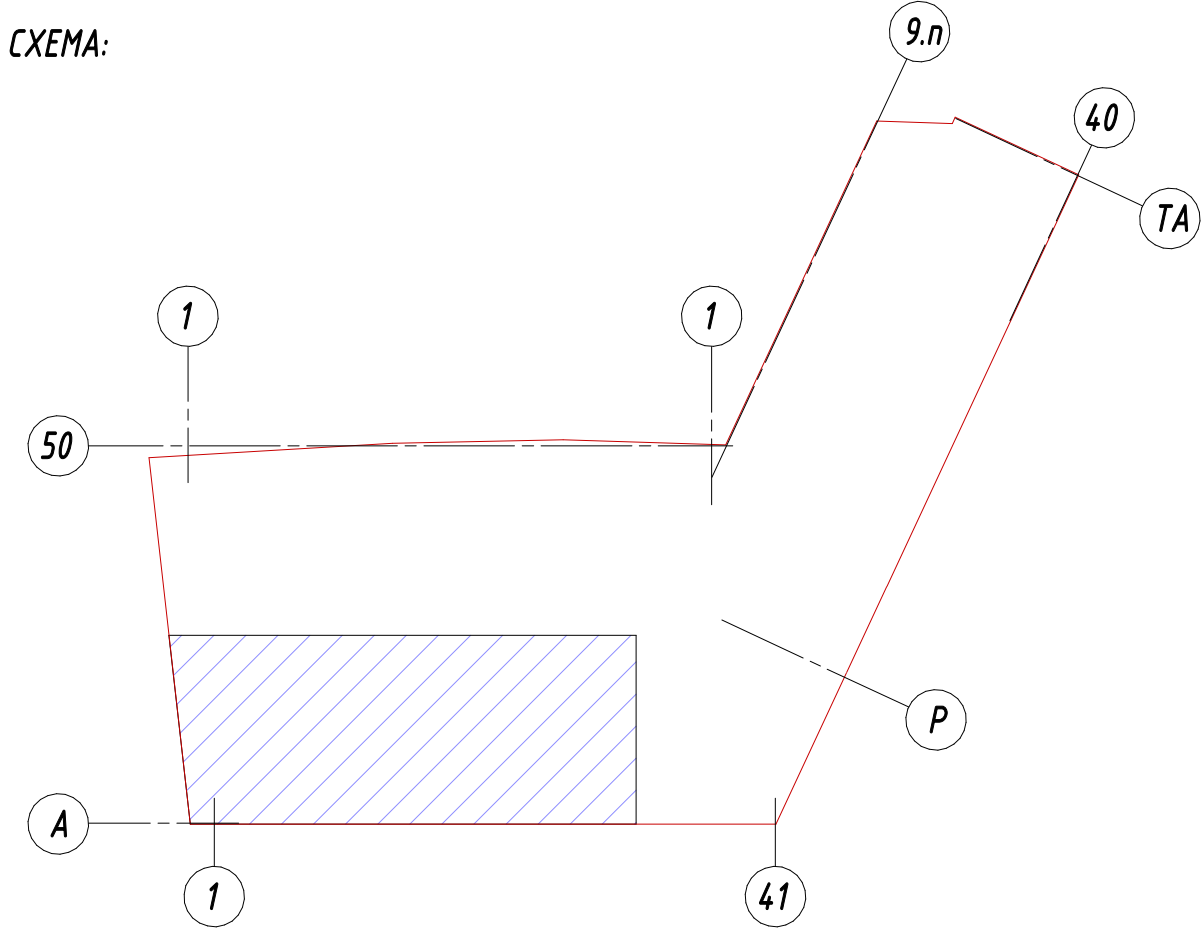

						УМО-РД-АСО					
						Многоэтажные многоквартирные жилые дома со встроенными помещениями и подземной автостоянкой на территории, ограниченной улицами Энтузиастов, Рудольфа Нуреева, Мусы Гареева в Октябрьском районе городского округа город Уфа Республики Башкортостан. Лист 1					
1	1	Зем.	1-26	<i>Леонова</i>	08.26	Архитектурные решения. Подземная часть			Стадия	Лист	Листов
Изм.	Кол.уч.	Лист	№ док	Подпись	Дата				Р	04	
Разраб.	Балабанова			<i>Балабанова</i>	08.26						
Рук.проекта	Ермолова			<i>Ермолова</i>	08.26						
Г.АП	Братошова			<i>Братошова</i>	08.26						
ГИП	Бренцис			<i>Бренцис</i>	08.26						
Н.контр.	Леонова			<i>Леонова</i>	08.26	Кладовый план. Фрагмент 2			М.К.3		
						М.КА указано					